


| LÉGENDE                  |  |
|--------------------------|--|
| Désignation              |  |
| Espaces verts            |  |
| Voirie existante         |  |
| Arbres hautes tiges      |  |
| Voirie                   |  |
| Trottoirs                |  |
| Places de stationnements |  |
| Espaces Verts            |  |
| Cheminements piétons     |  |
| Résine gravillonnée      |  |
| Bordure T2 Haute         |  |
| Bordure T2 Basse         |  |
| Bordure P1               |  |
| Caniveau CS1             |  |

| LÉGENDE COUPE A- A |  |
|--------------------|--|
| Désignation        |  |
| Enrobés, 5cm       |  |
| Pavés Béton, 7cm   |  |
| GNT 0/20, 15 cm    |  |
| GNT 0/31.5         |  |
| Sol support        |  |
| Fouilles           |  |

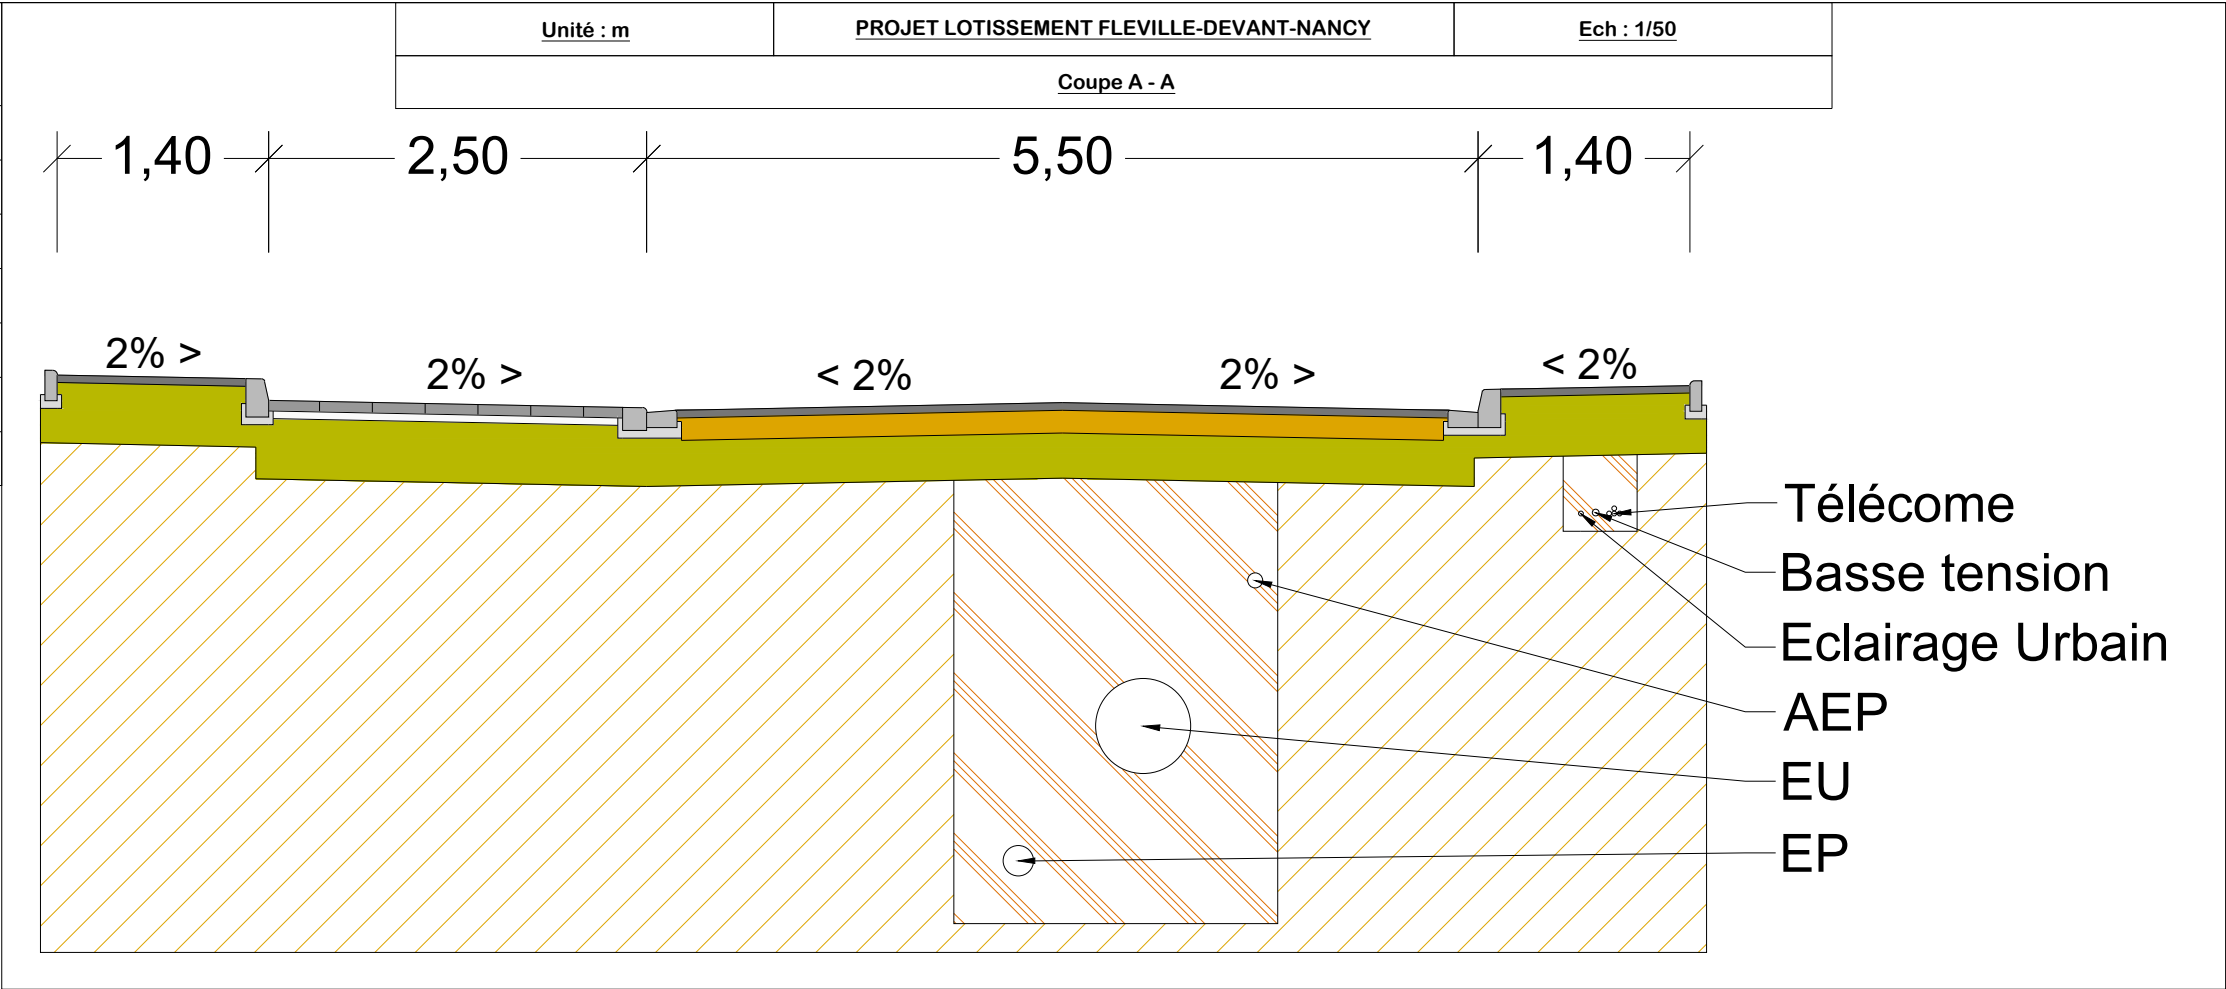

|                       |                                          |               |
|-----------------------|------------------------------------------|---------------|
| Ech : 1/500           | IUT NANCY-BRABOIS - SAE 5.02             | Julien Pulhuj |
| Unité : m             | PROJET LOTISSEMENT FLEVILLE-DEVANT-NANCY | 12/11/2025    |
| PLAN DE PROJET VOIRIE |                                          |               |